


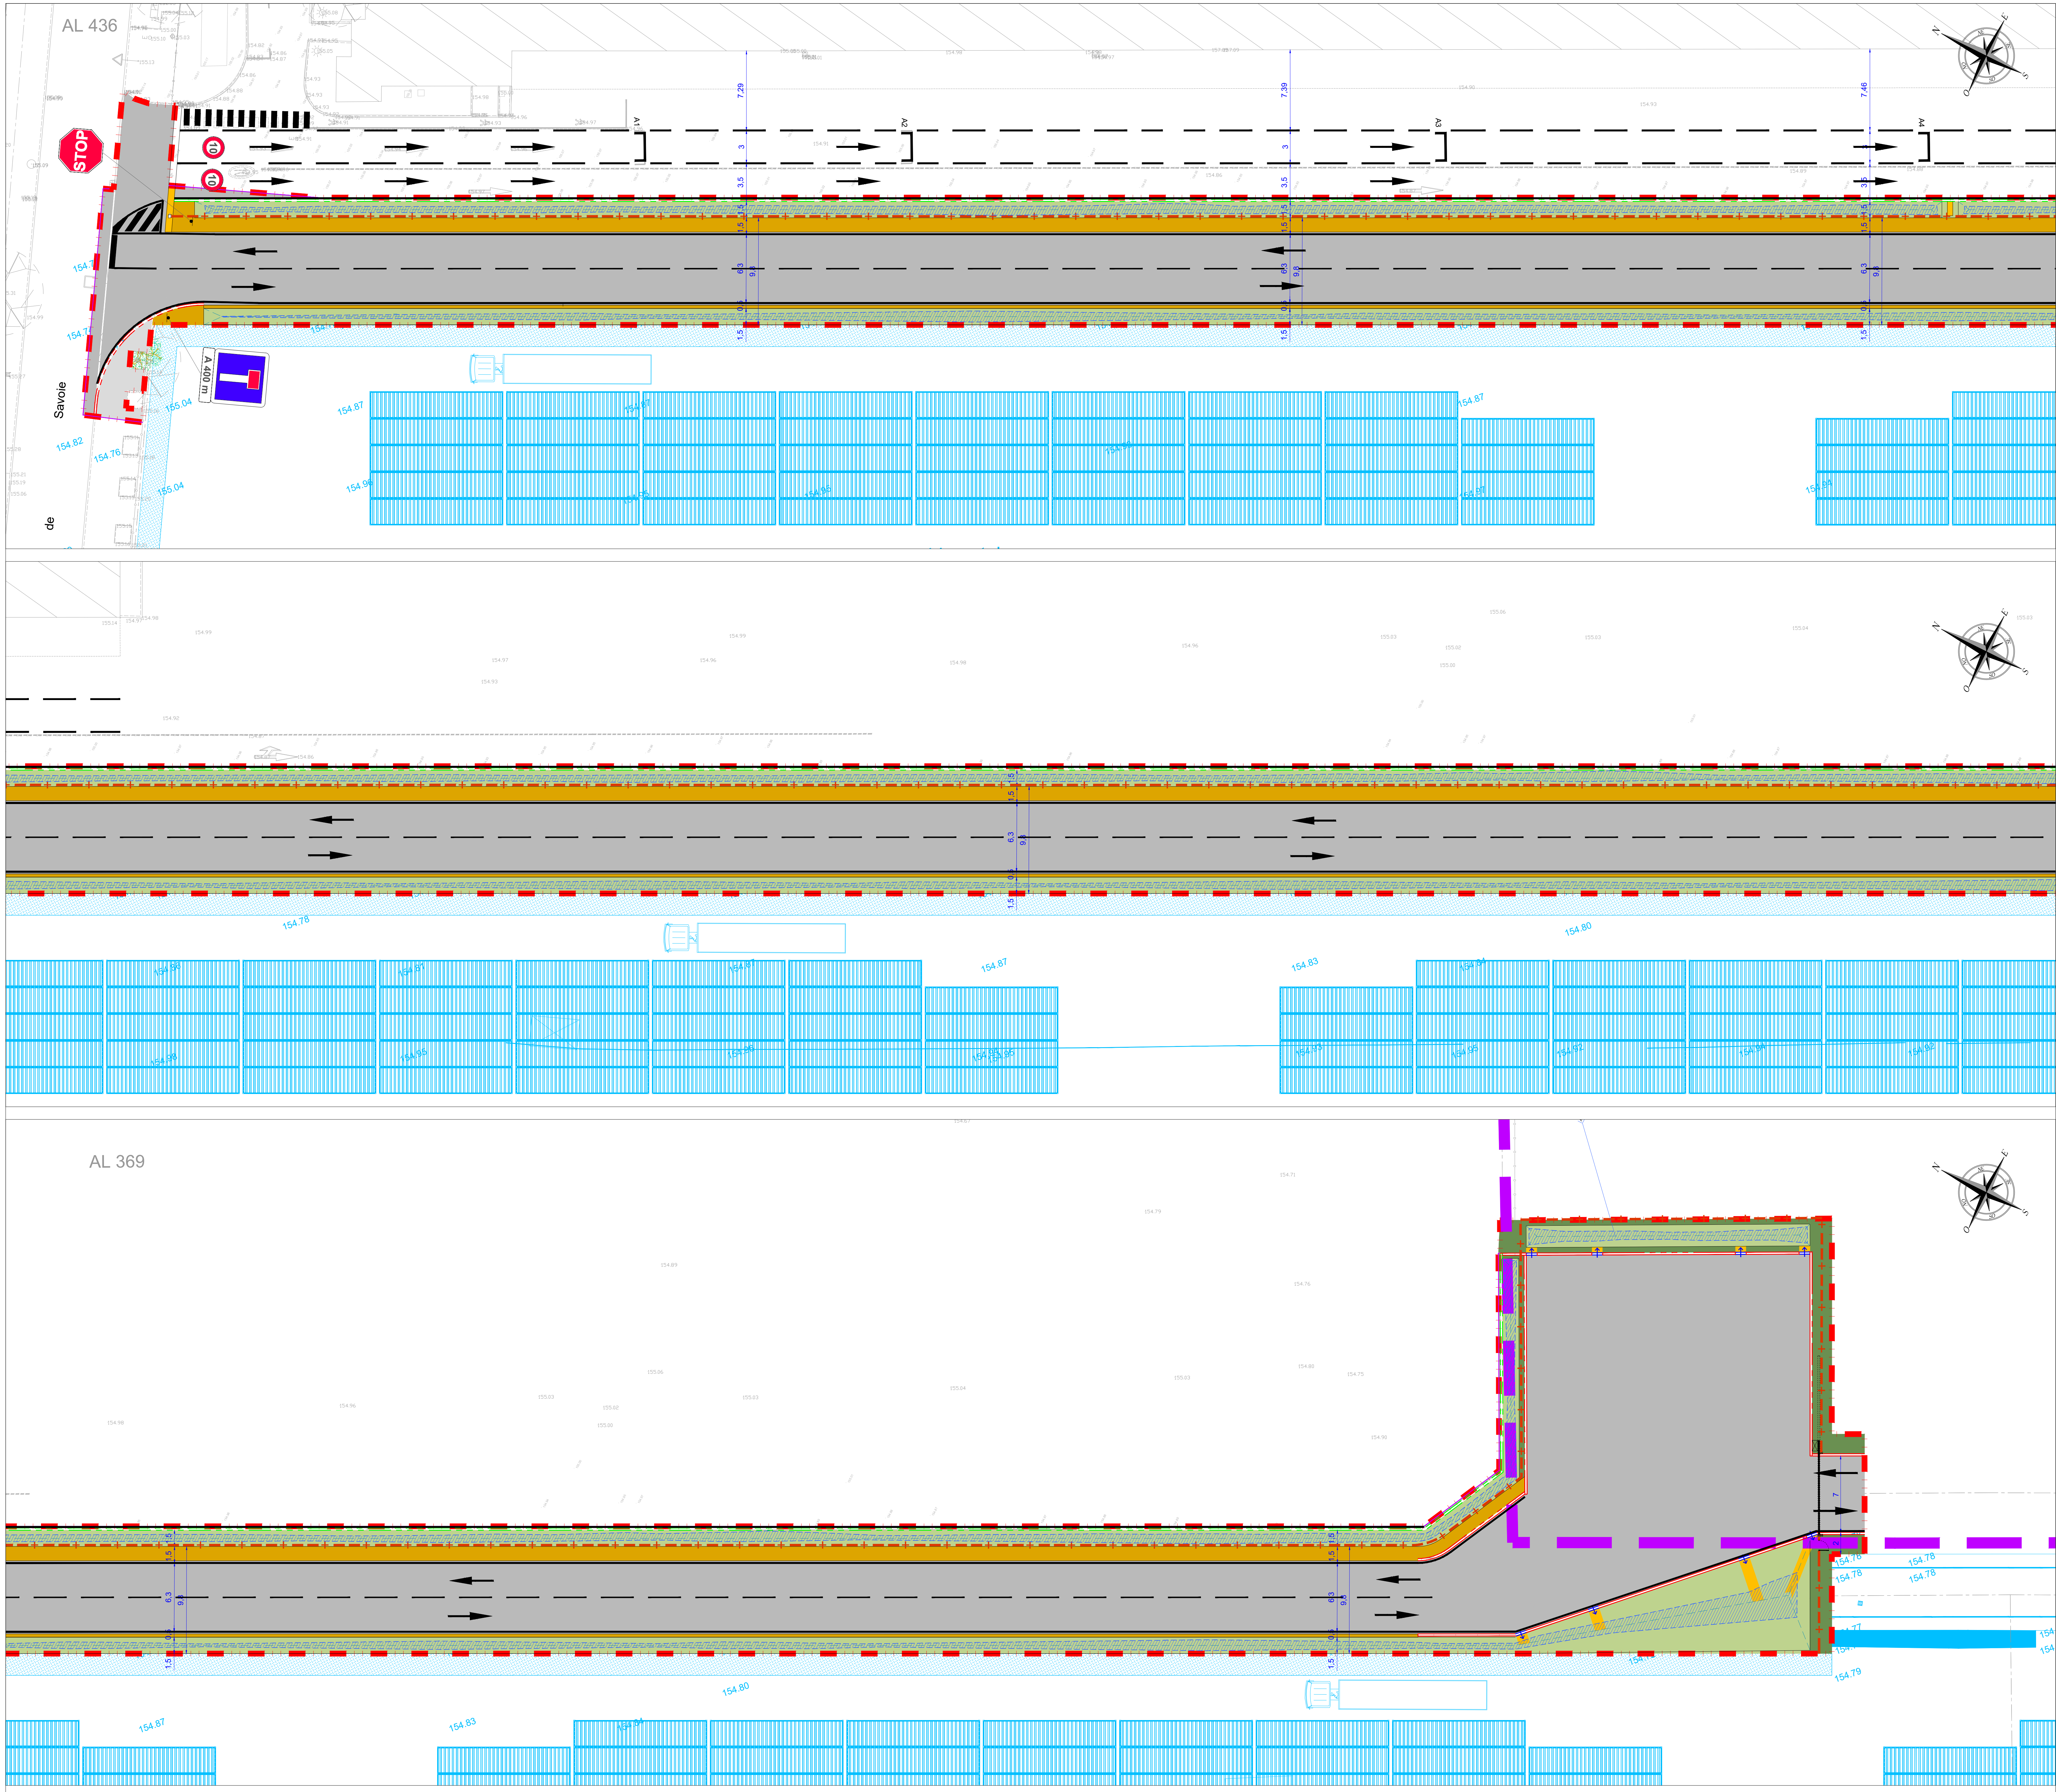

LEGENDE

Voirie

GENERALITES

- Cotations
 - Voirie - Filaire
 - Périmètre du projet
 - Périmètre projet
 - SERFIM RECYCLAGE
 - Périmètre projet
 - COMBRONDE
- BORDURES**
- Bordure Noyée T2_vue 0cm
 - Bordure Haute T3_vue 14cm
 - Bordure Haute T3_AVALOIR_vue 14cm

REVETEMENTS

- Trait de sciage revêtement existant
- Chaussée - Enrobé Noir
- Chaussée - Béton
- Accotement stabilisé non revêtu 0/31.5

ESPACES VERTS

- Espace vert
- Noue paysagère engazonnée

MOBILIER URBAIN

- Poteau de renfort pour portail coulissant entrée MAYAJ (IPN 120 minimum / massif béton)
- Clôture rigide
- Portail Coulissant (Hors marché)
- Portillon (Hors marché)

SIGNALISATION HORIZONTALE

- Ligne continue _3u=15
- Ligne type T3 _3u=15
- Ligne Stop
- Flèches directionnelles
- Passage piétons
- Zébra
- Ligne blanche_Indicateur d'arrêt PL_3u=15
- Lettrage zone d'arrêt
- Peinture type panneau B14_10

SIGNALISATION VERTICALE

- Mât supportant les panneaux

TYPE AB

- AB4

TYPE C

- C13 A

TYPE M

- M1

Indice	Date	Modifications	Etébli	Vérifié / Validé
A	AVRIL 2026	Première diffusion	JL	DF
B	MAI 2026	Modifications suite à la réunion du 18.05.2026 avec le client	JL	DF

MAITRISE D'OUVRAGE Compagnie Nationale du Rhône	1, Rue de Chalon sur Saône 69002 LYON	EMETTEUR EGIS LYON	Intervalle Le Carat 135 Avenue Tassin 69127 BRON Cedex 06
			

REALISATION DE LA DESSERTE
ROUTIERE DE LA PARCELLE SERFIM
DU SITE PORTUAIRE DE LOIRE-SAINT-ROMAIN

PG200
PLAN DE REVETEMENTS, SIGNALISATIONS

Identification fichier : EGIS_CN88_PRO_PLAN D'AMENAGEMENT_B							
Opération	Classement	Propriétaire	Code métier	Type document	Discrétisation	Phase	Numéro Chrono
CNR		MOE	VRD	PLN		PRO/DCE	B
Date : JUIN 2026		Format : A0					
Nivellement : NGF IGN 69		Sys.coord.Projection : RGF93-CC49				Echelle : 1:200	

Ce document est la propriété de Norm MCA. Toute diffusion ou reproduction intégrale ou partielle faite sans l'autorisation préalable et écrite à Norm MCA est interdite.